

POLITECNICO DI MILANO SCUOLA DEL DESIGN C.L. DESIGN DEGLI INTERNI PROGETTO:

HEMNES_102-426-35

RSO:
STRUMENTI E METODI
DEL PROGETTO

MARCO FERRARA

STUDENTI:
FRANCESCA MEZZANO

OGGETTO: HEMNES_102-426-35

NOTE:

NOME FILE:

HEMNES_102-426-35.dwg


VERS


-


A YYYY.MM.DD


TAVOLA NO.: 1 DI 3


DATA: 7/4/2017 SCALA: 1:20 REV: A FORMATO: A1 10 0.5m 11.25m 2.5m

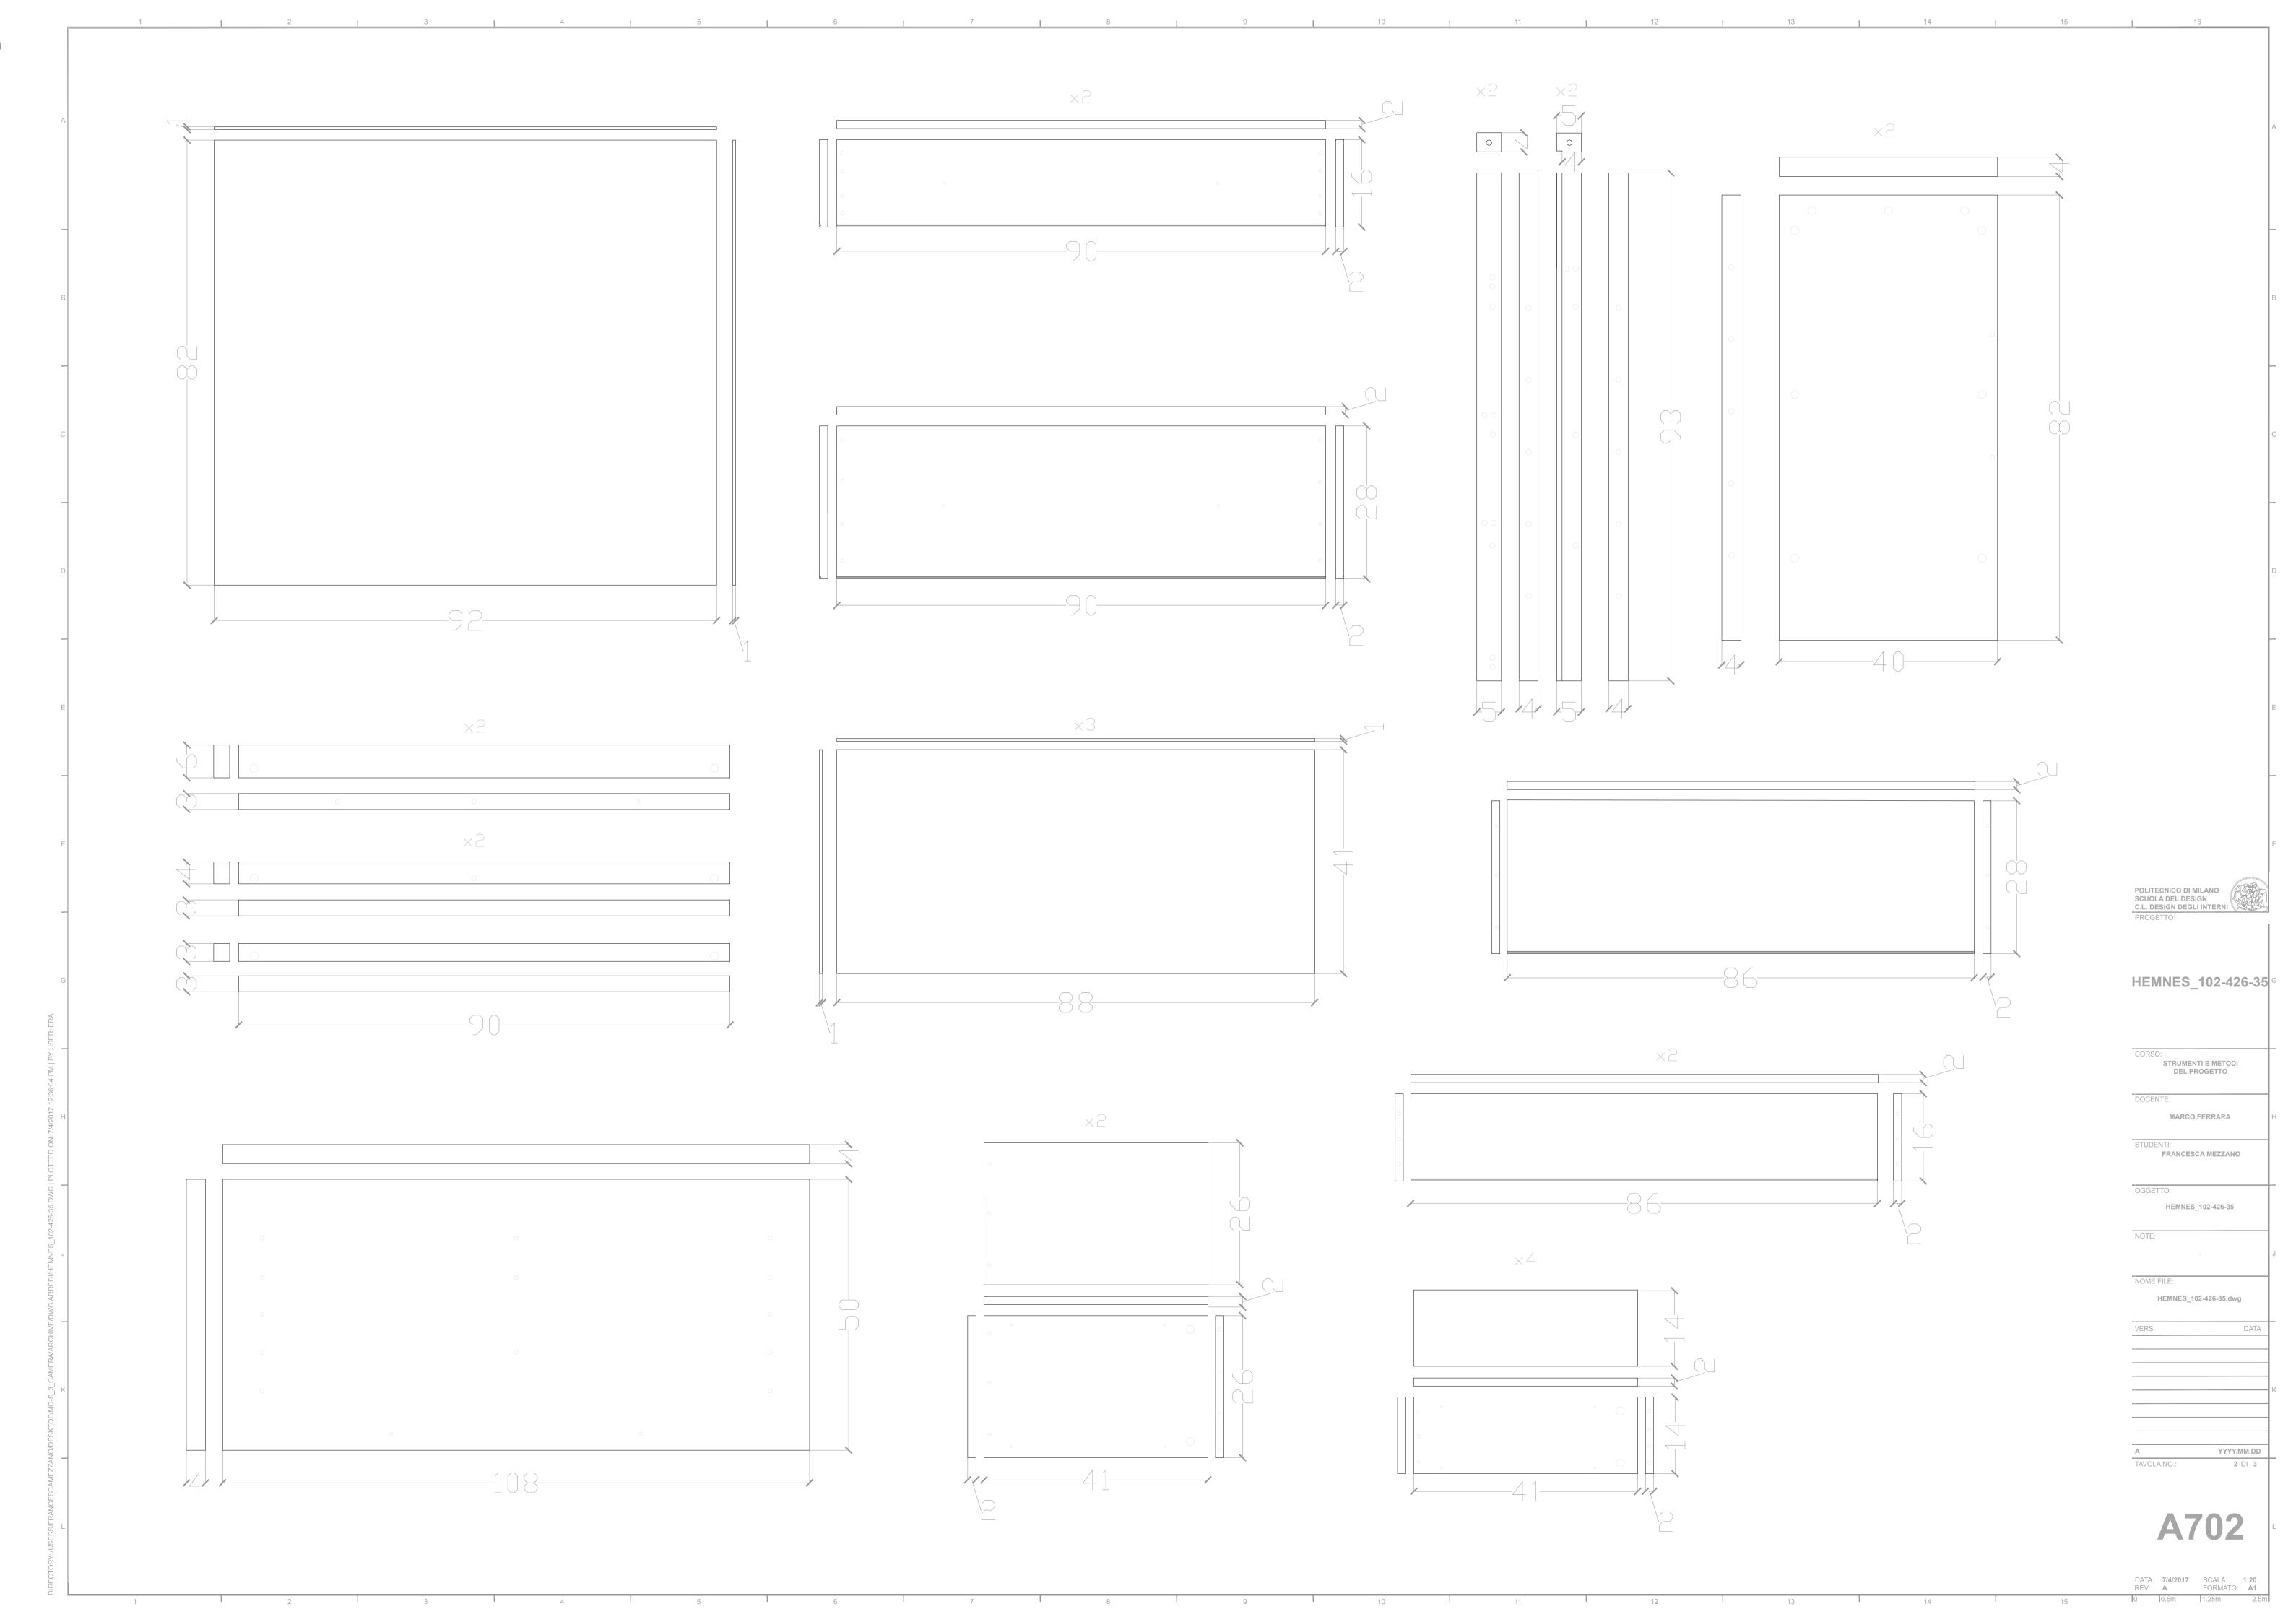

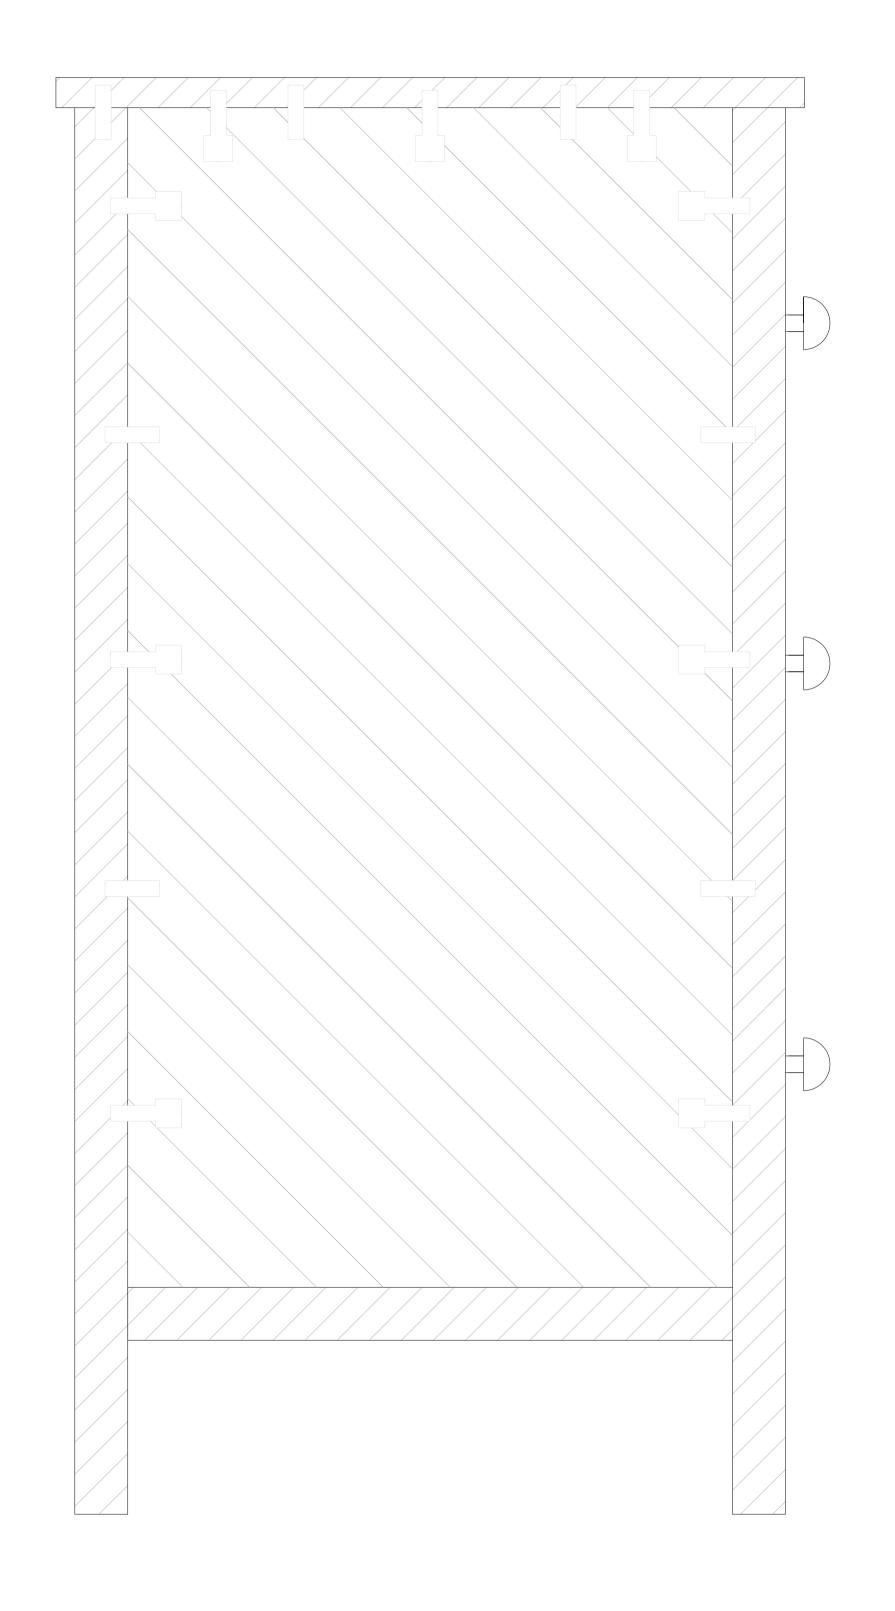

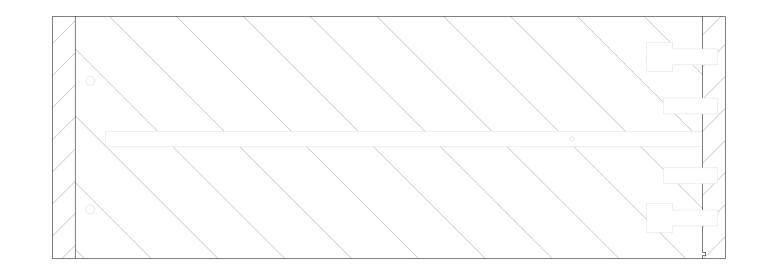

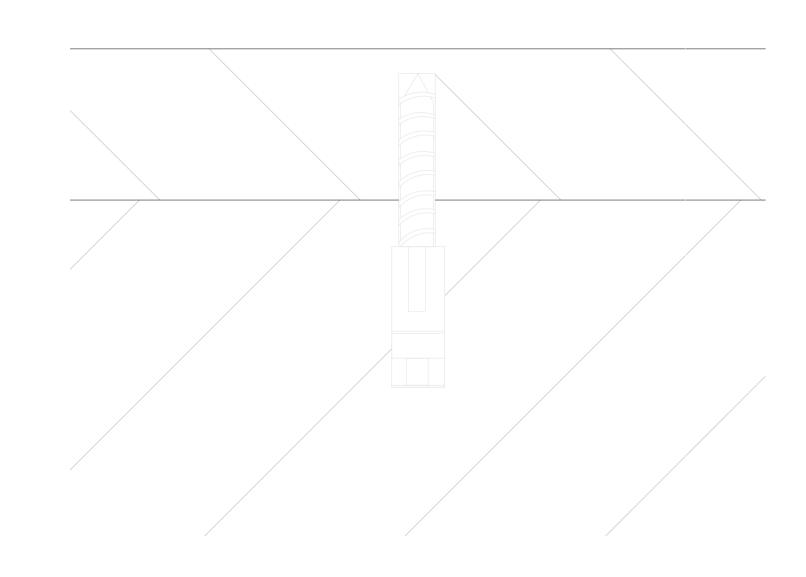

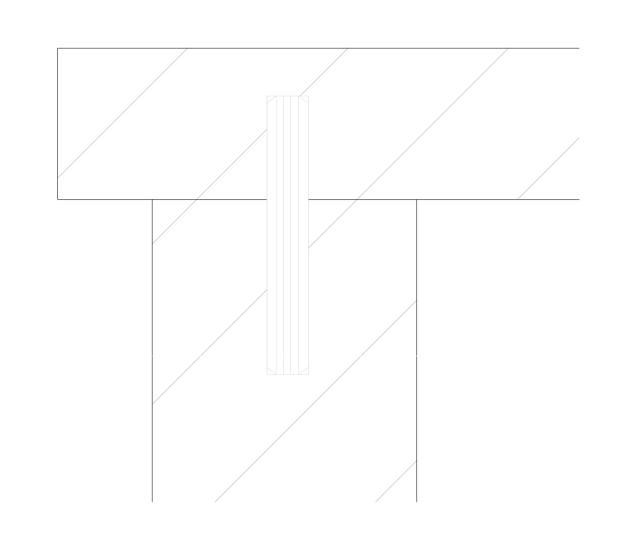

POLITECNICO DI MILANO
SCUOLA DEL DESIGN
C.L. DESIGN DEGLI INTERNI
PROGETTO:

HEMNES_102-426-35 G

ORSO:
STRUMENTI E METODI
DEL PROGETTO

MARCO FERRARA

STUDENTI:
FRANCESCA MEZZANO

OGGETTO:
HEMNES_102-426-35

NOTE:

NOME FILE:
HEMNES_102-426-35.dwg

....

A YYYY.MM.DD

TAVOLA NO.: 3 DI 3

Α703

DATA: 7/4/2017 SCALA: 1:20 REV: A FORMATO: A1 0 0.5m 11.25m 2.5m